


PLANO EJECUTIVO: PLANTA ARQUITECTÓNICA

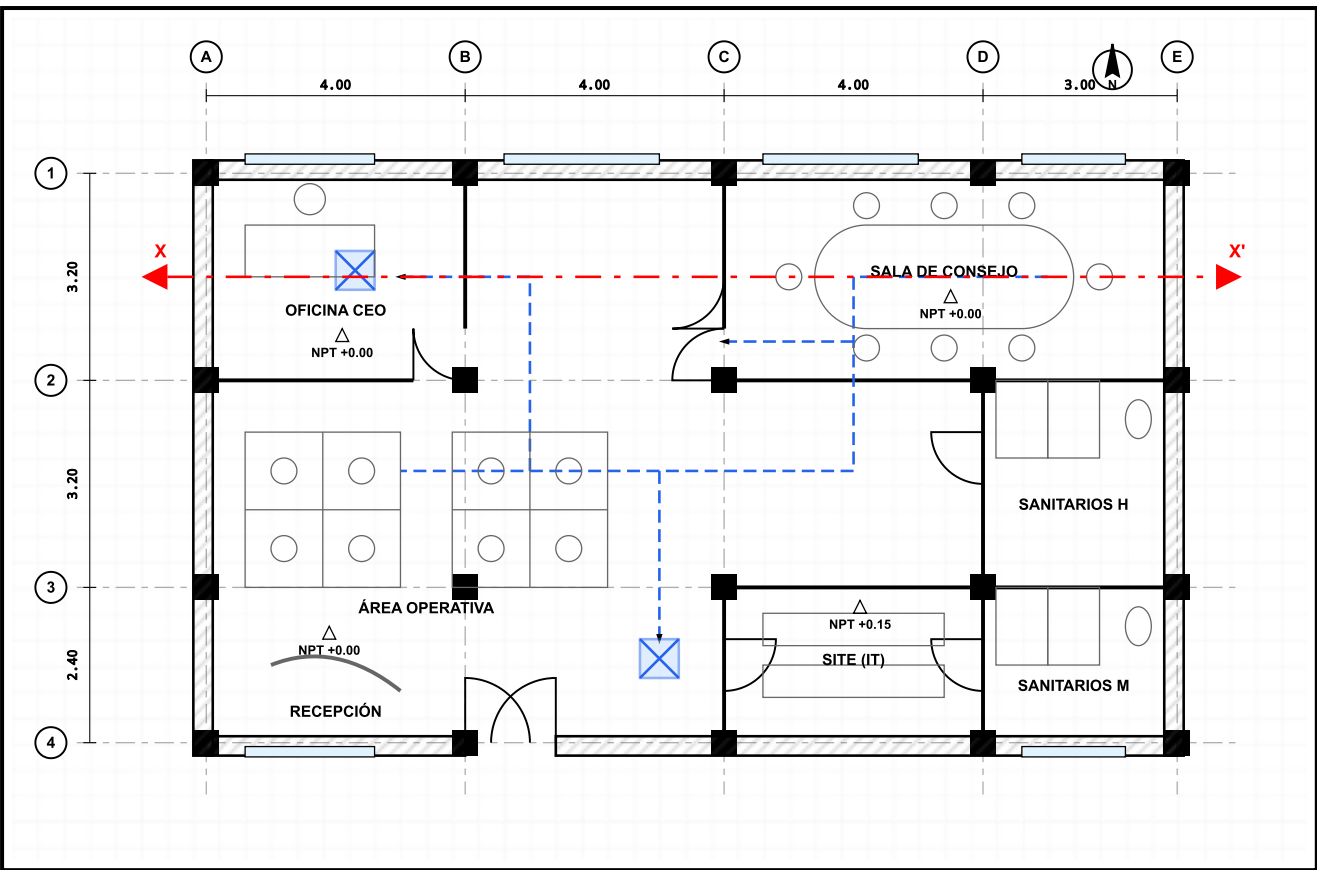

PROYECTO OFICINAS CORPORATIVAS "TORRE SUR"	PLANO PLANTA ARQUITECTÓNICA - NIVEL 4	ESCALA 1:50 (REF)	FECHA OCT 2026	CLAVE ARQ-01
--	---	-----------------------------	--------------------------	------------------------

Muro de Carga / Estructural	Muro Divisorio Ligero	Ductos HVAC
Línea de Corte Transversal		

CUADRO DE ACABADOS (ESPECIFICACIONES)

El siguiente cuadro vincula las zonas indicadas en la planta arquitectónica (ARQ-01) con los materiales, revestimientos y especificaciones constructivas a instalarse. Los niveles están referenciados al banco de nivel del núcleo de elevadores (NPT +0.00).

ESPACIO	PISOS (NPT)	MUROS (ACABADO FINAL)	PLAFONES (CIELO RASO)	ZOCLO
Recepción	Mármol Travertino formato 60x120cm (NPT +0.00).	Panelado de madera de nogal americano (M-01) y pintura vinílica blanca.	Falso plafón de tablaroca con cajillos iluminados (H: 2.80m).	Madera 10cm.
Oficina CEO	Alfombra modular acústica 50x50cm, gris oxford (NPT +0.00).	Pintura vinílica tipo mate (M-02) / Cristal templado acústico 12mm hacia pasillo.	Plafón reticular acústico 60x60cm Armstrong (H: 2.60m).	Aluminio natural.
Sala Consejo	Alfombra modular alto tráfico (NPT +0.00).	Muros con paneles fonoabsorbentes PET ranurado y pintarrón de cristal esmerilado.	Falso plafón liso con suspensión acústica oculta (H: 2.70m).	Aluminio natural.
Área Operativa	Piso vinílico en rollo (LVT) acabado concreto pulido (NPT +0.00).	Pintura vinílica blanca en muros perimetrales. Tablaroca lisa.	Losa aparente (Sin plafón), instalaciones expuestas, pintura negra mate.	Vinílico 7cm.
Site (IT)	Piso técnico elevado 15cm c/ losetas modulares antiestáticas (NPT +0.15).	Pintura epóxica retardante de fuego.	Losa aparente sellada.	No aplica.
Sanitarios	Porcelanato rectificado antideslizante 45x90cm (NPT +0.00).	Cerámico vidriado de piso a techo en áreas húmedas, color gris claro.	Plafón liso resistente a humedad tipo tablaroca verde (H: 2.40m).	Cerámico 10cm.

ESPECIFICACIONES DE CARPINTERÍA Y CANCELERÍA

CLAVE	TIPO	ANCHO	ALTO	DESCRIPCIÓN TÉCNICA
P-01	Puerta Doble	1.80 m	2.20 m	Puerta de cristal templado 12mm con herrajes de acero inoxidable, abatimiento dual. Sistema cierra puertas hidráulico en piso (Acceso).
P-02	Puerta Sencilla	0.90 m	2.20 m	Puerta de tambor en chapa de nogal con relleno acústico de lana mineral. Cerradura de manija marca Yale. (Oficinas/Site).
C-01	Cancel Fijo	Variable	2.60 m	Muro de cristal templado 10mm montado sobre perfiles perimetrales de aluminio anodizado natural en formato 'U'.
V-01	Ventanal ext.	Variable	2.80 m	Fachada integral de aluminio serie 70 con cristal doble insulated (Duo-Vent) con control solar Low-E.

NOTAS GENERALES DE CONSTRUCCIÓN:

- Las cotas rigen sobre el dibujo. No medir a escala en obra.
- El contratista deberá verificar todas las medidas en sitio antes de la fabricación de cancelería o mobiliario a la medida.
- Cualquier discrepancia entre los planos arquitectónicos y los planos de instalaciones (MEP) deberá ser consultada con el Director Responsable de Obra (DRO) previo a la ejecución.